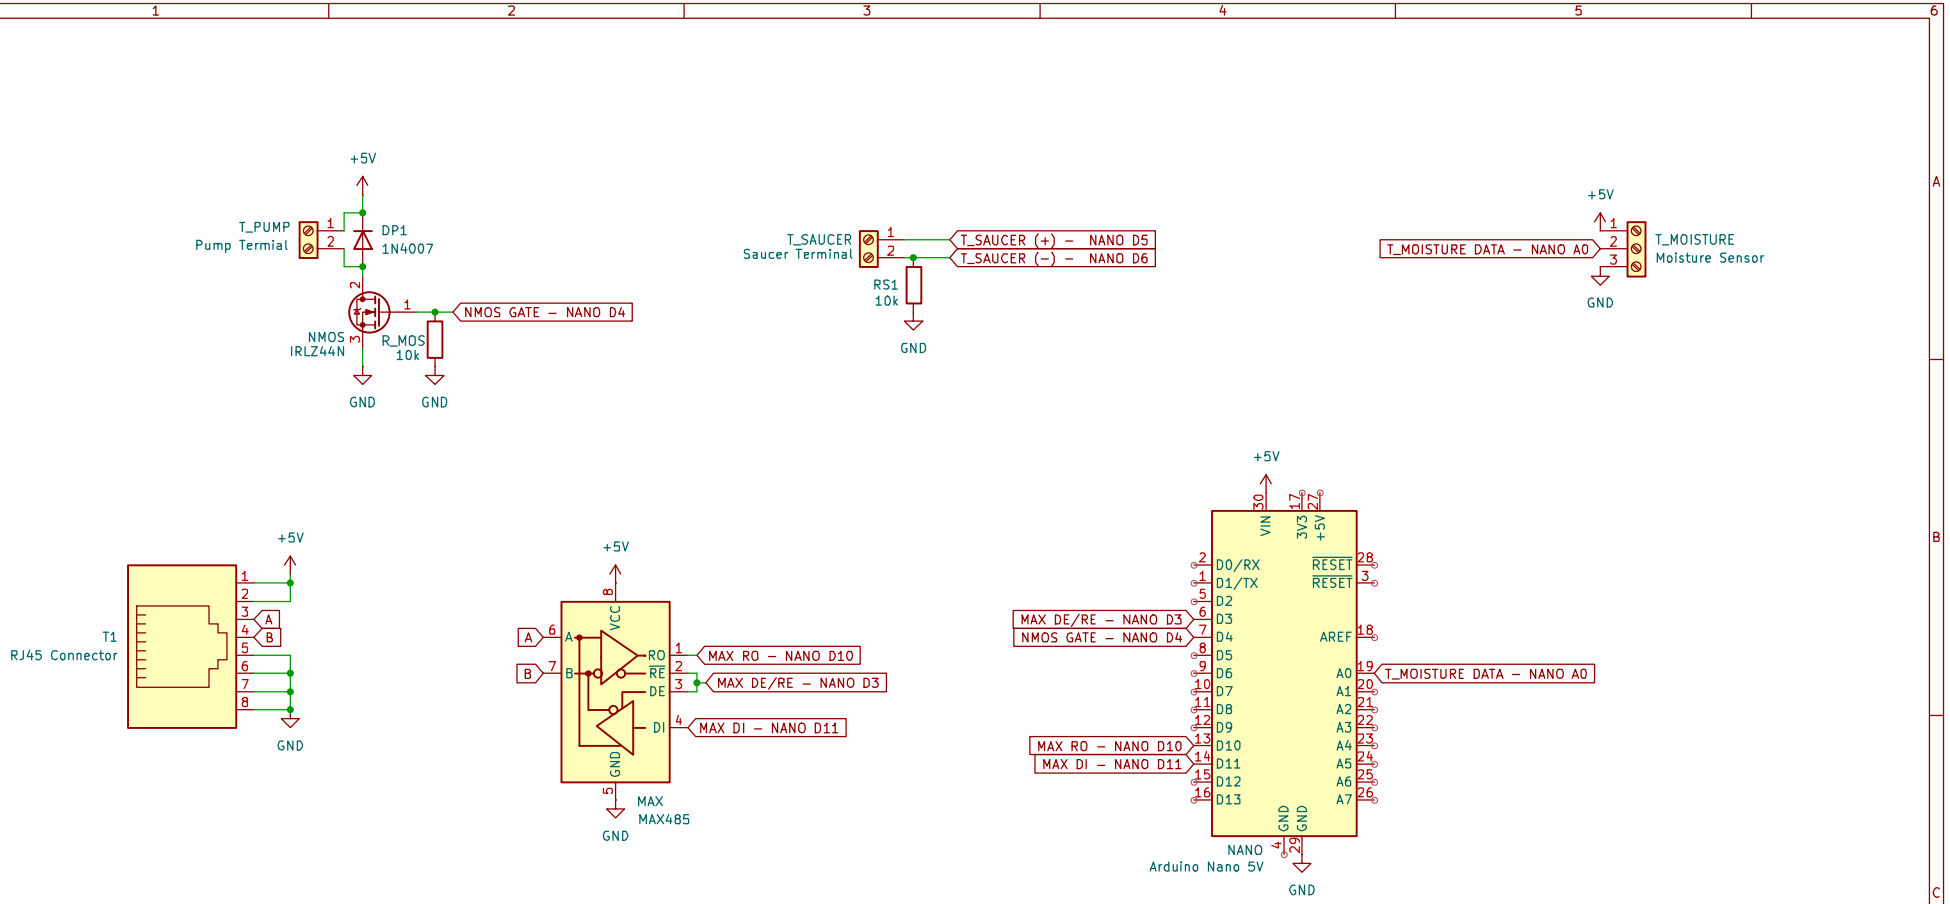

Sheet: /
File: plant_unit.kicad_sch

Title: Plant Unit Electrical Scheme

Size: A4	Date: 2025-07-21	Rev:
KiCad E.D.A. 8.0.3		Id: 1/1